

ROOF NOTES

1. Roofing to be installed per manufacturer's specifications including installation of all required flashing.
2. Flash the top of exterior openings (doors, windows, etc.) with 26 ga. sheet metal. Wrap bottom and sides with one full-length piece of waterproof building paper and tape per manufacturer's specifications. It is recommended that window installation be inspected and approved by window representative to validate warranty.
3. Flash fill roof penetrations and junctions of roofing with vertical surfaces.
4. Install gutters and downspouts as shown on plans. Consult with architect if larger gutters and/or additional downspouts are recommended.
5. Roofer shall confirm with plumber and mechanical contractors that all roof jacks and vents are placed in the least visible locations prior to applying roofing.
6. Spray foam insulation does not require attic ventilation
7. All roofing and assembly material shall be Class A Fire rated
8. All roof gutters shall be provided with an approved means to prevent the accumulation of leaves and debris as required by Wildland-Urban Interface, Chapter 7A CBC.
9. Metal flashing @ roof valleys shall consist of 26 ga. sheetmetal installed over a min.36" wide underlayment of T2# cap sheet running the entire length of the valley.
10. Class A rated Ice & Water shield underlayment shall comply with ASTM D226 Type I; ASTM D4869 Type I,II,III or IV; ASTM D6757 and shall bear label indicating compliance to standard.
11. Soffit and eave materials must be non-combustible or ignition-resistant and vents less than 12" above ground or walking surface must be approved to resist intrusion of flame and burning embers.
12. Operable skylights shall be protected by a non-combustible mesh screen with openings not to exceed 1/8".

County of Santa Cruz
Community Development & Infrastructure
Reviewed for Code Compliance
By: GJJ
Date: 8/8/2024
Permit: APP-231007*
CCD/DEF: N/A

These documents are the property of Michael Vierhus Architect and shall not be used or reproduced in anyway without his consent.

Michael Vierhus
ARCHITECT
P.O.Box 1098 Los Gatos CA 95031
408.867.5808




Michael Vierhus




ARCHITECTURAL PLANS FOR:
STEVE & MICHELLE BELL
40 BLOSSOM WAY SCOTTS VALLEY CA
APN 056-131-09

printed 5/20/2024
revisions

sheet
A-4

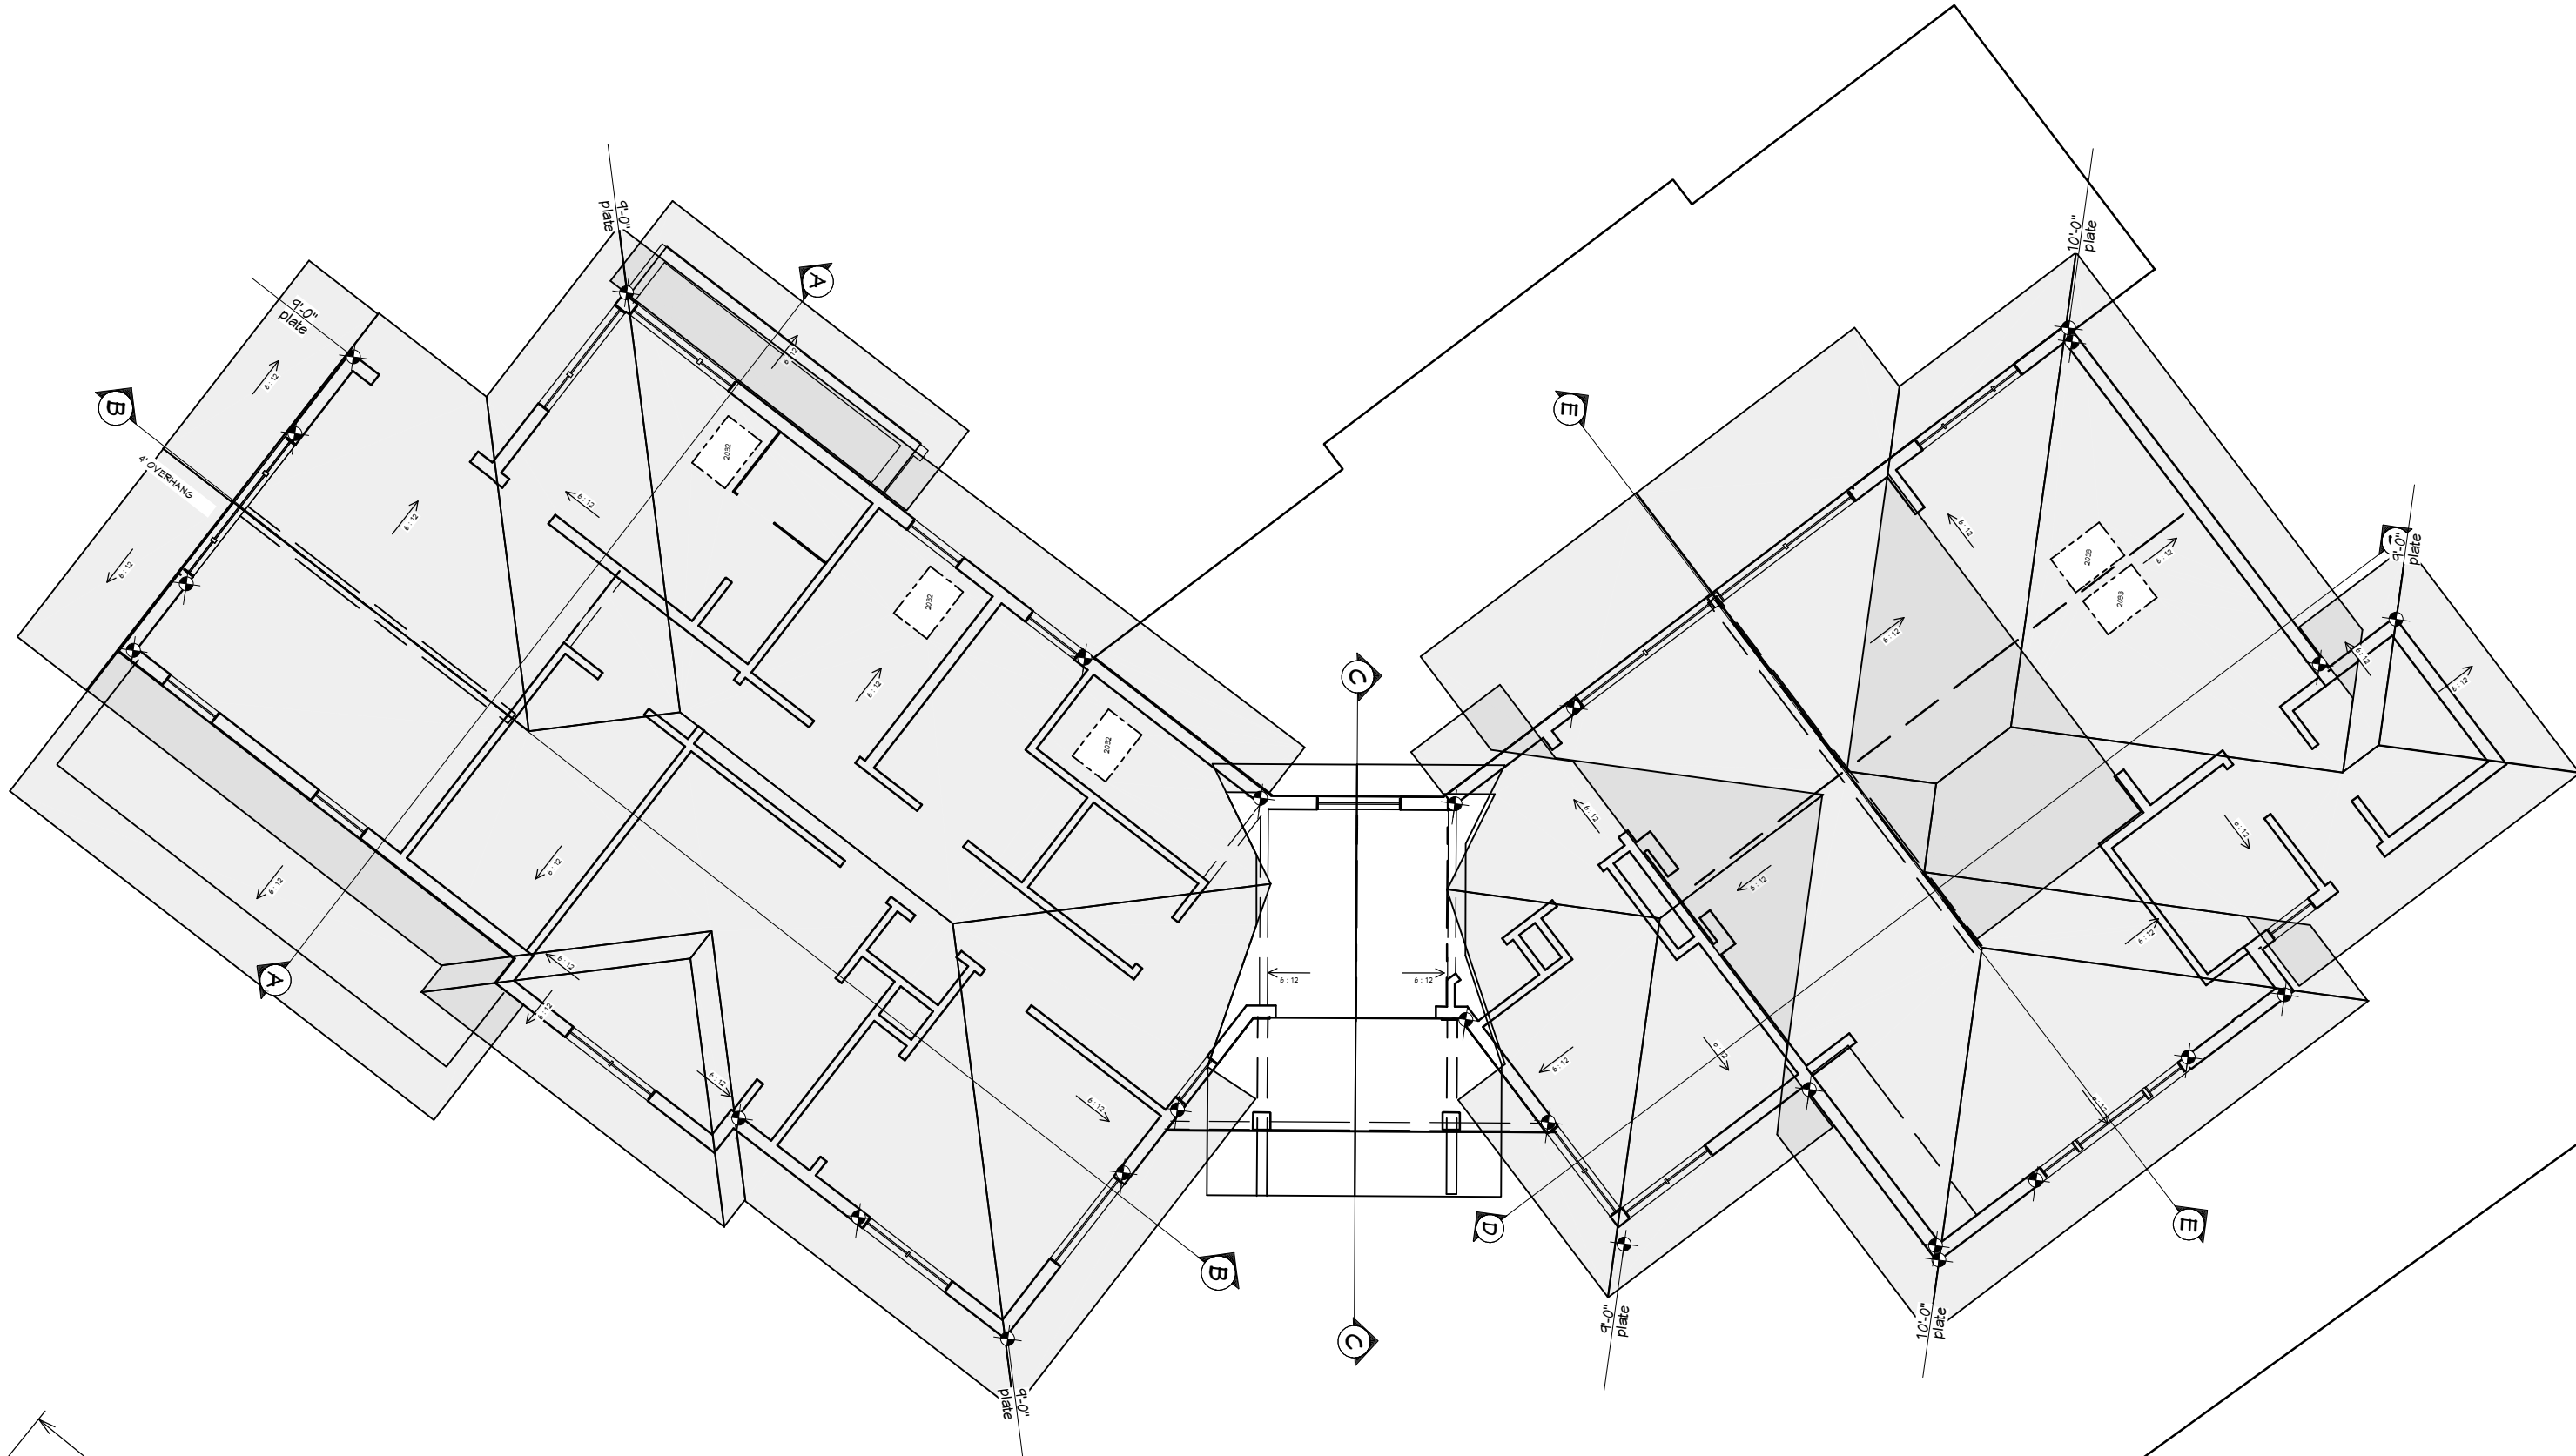

ROOF PLAN
1/8"=1'-0"

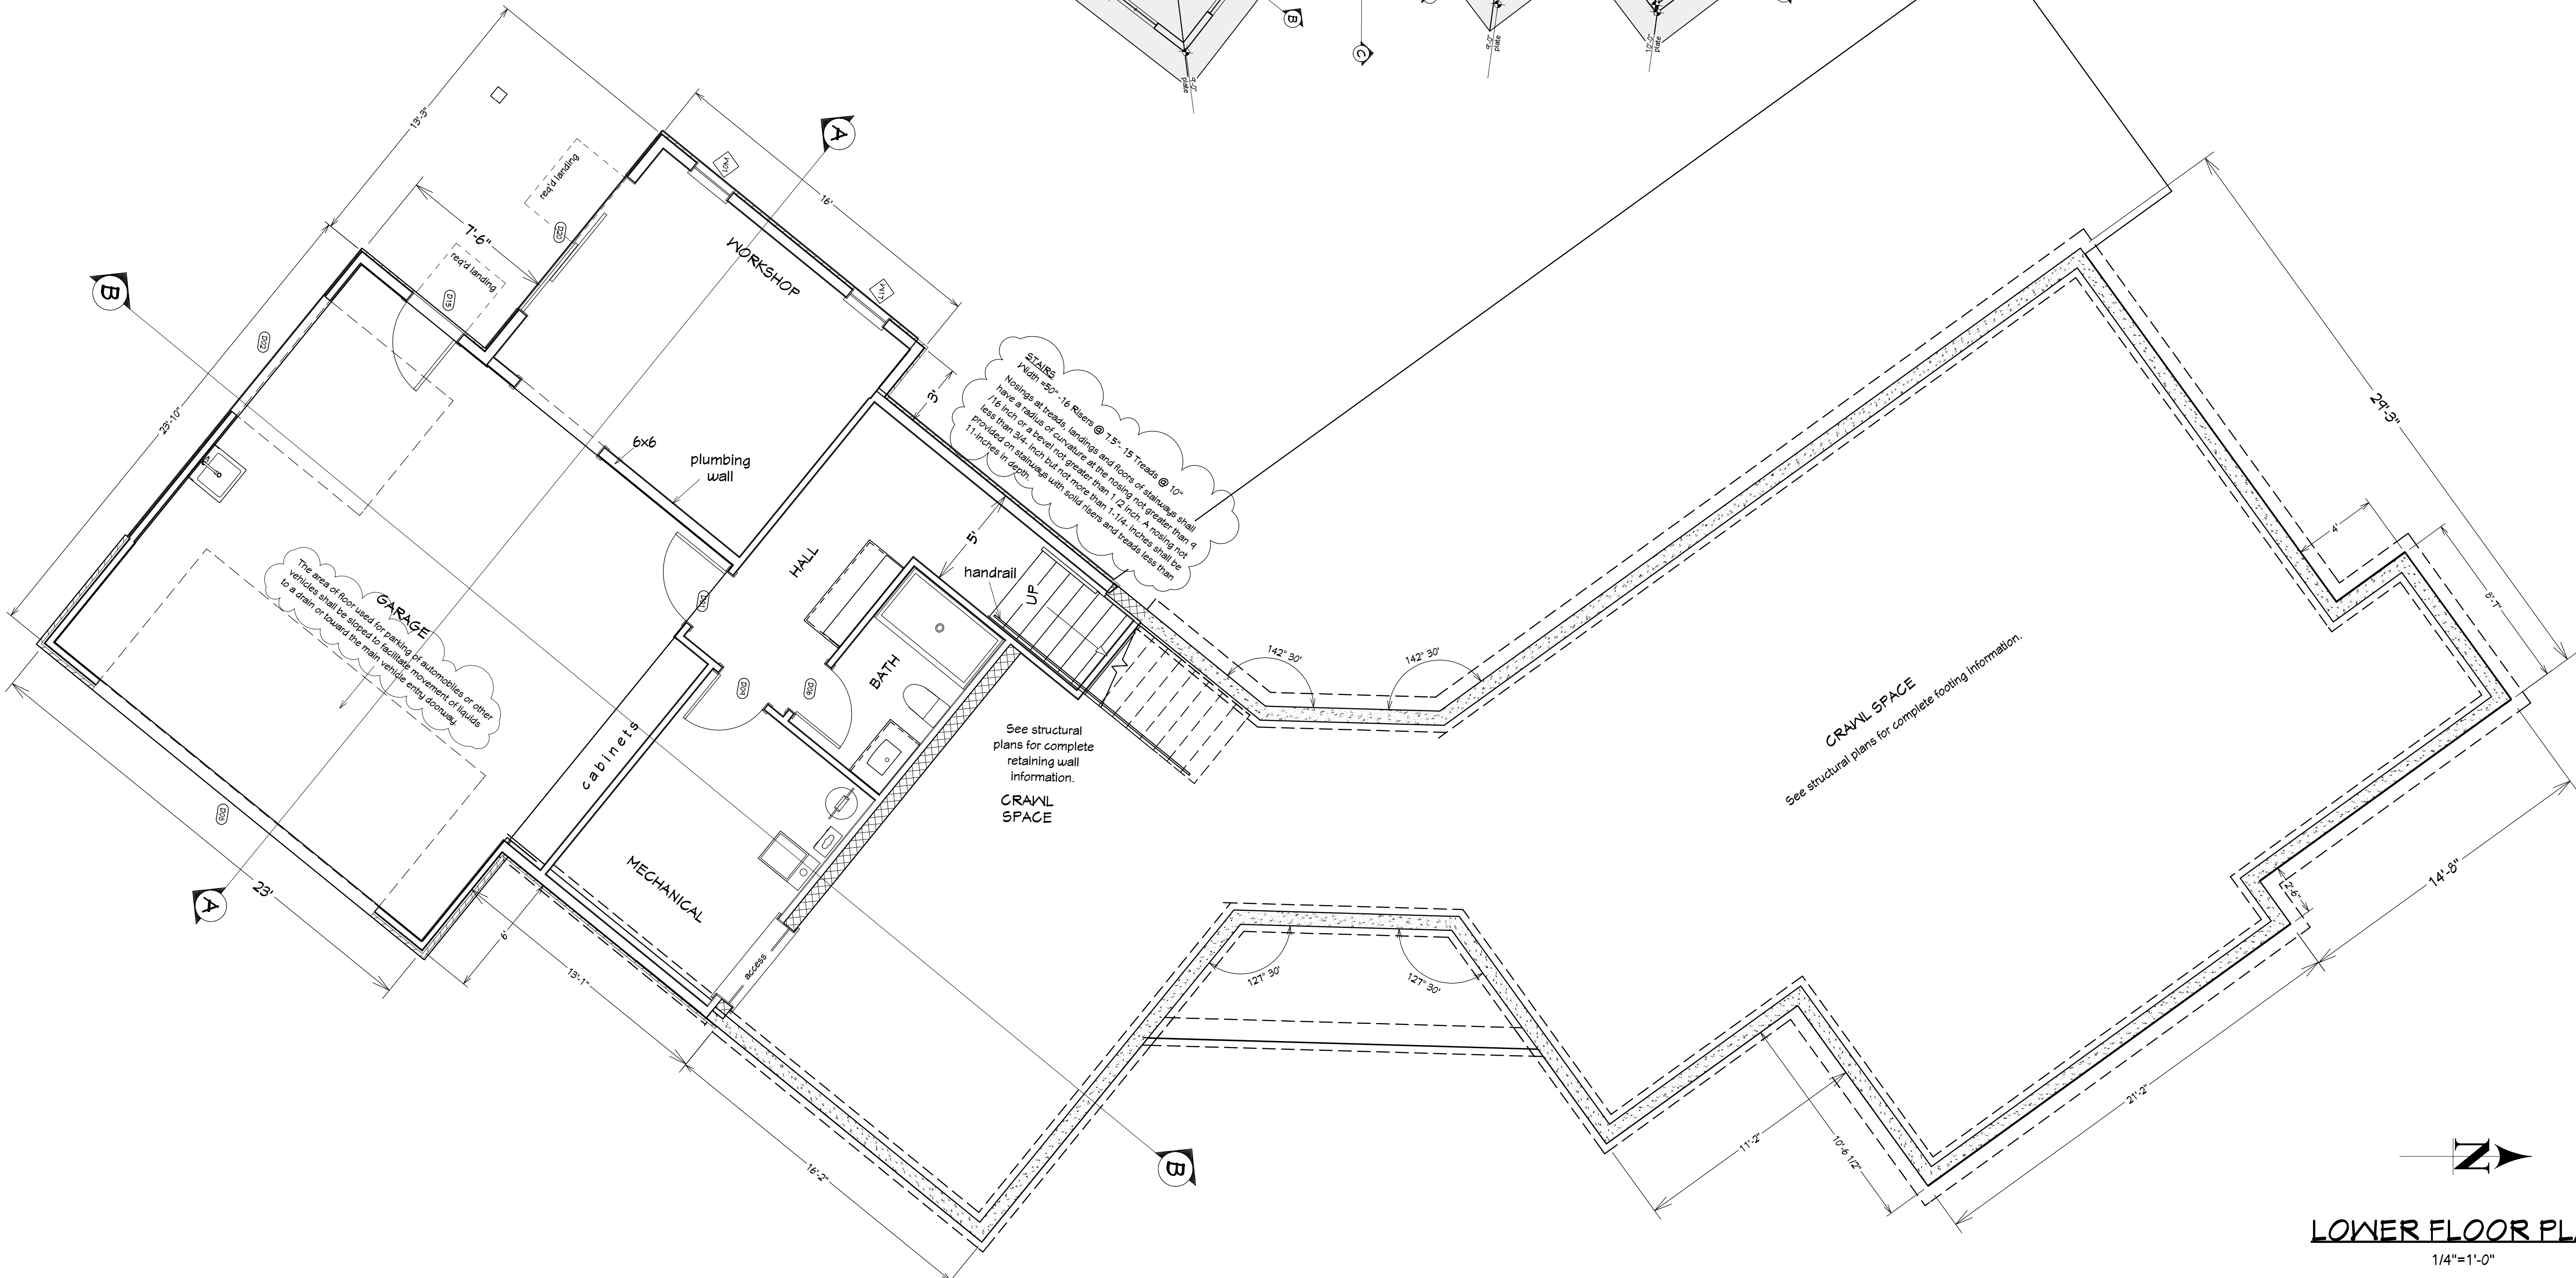

LOWER FLOOR PLAN
1/4"=1'-0"