

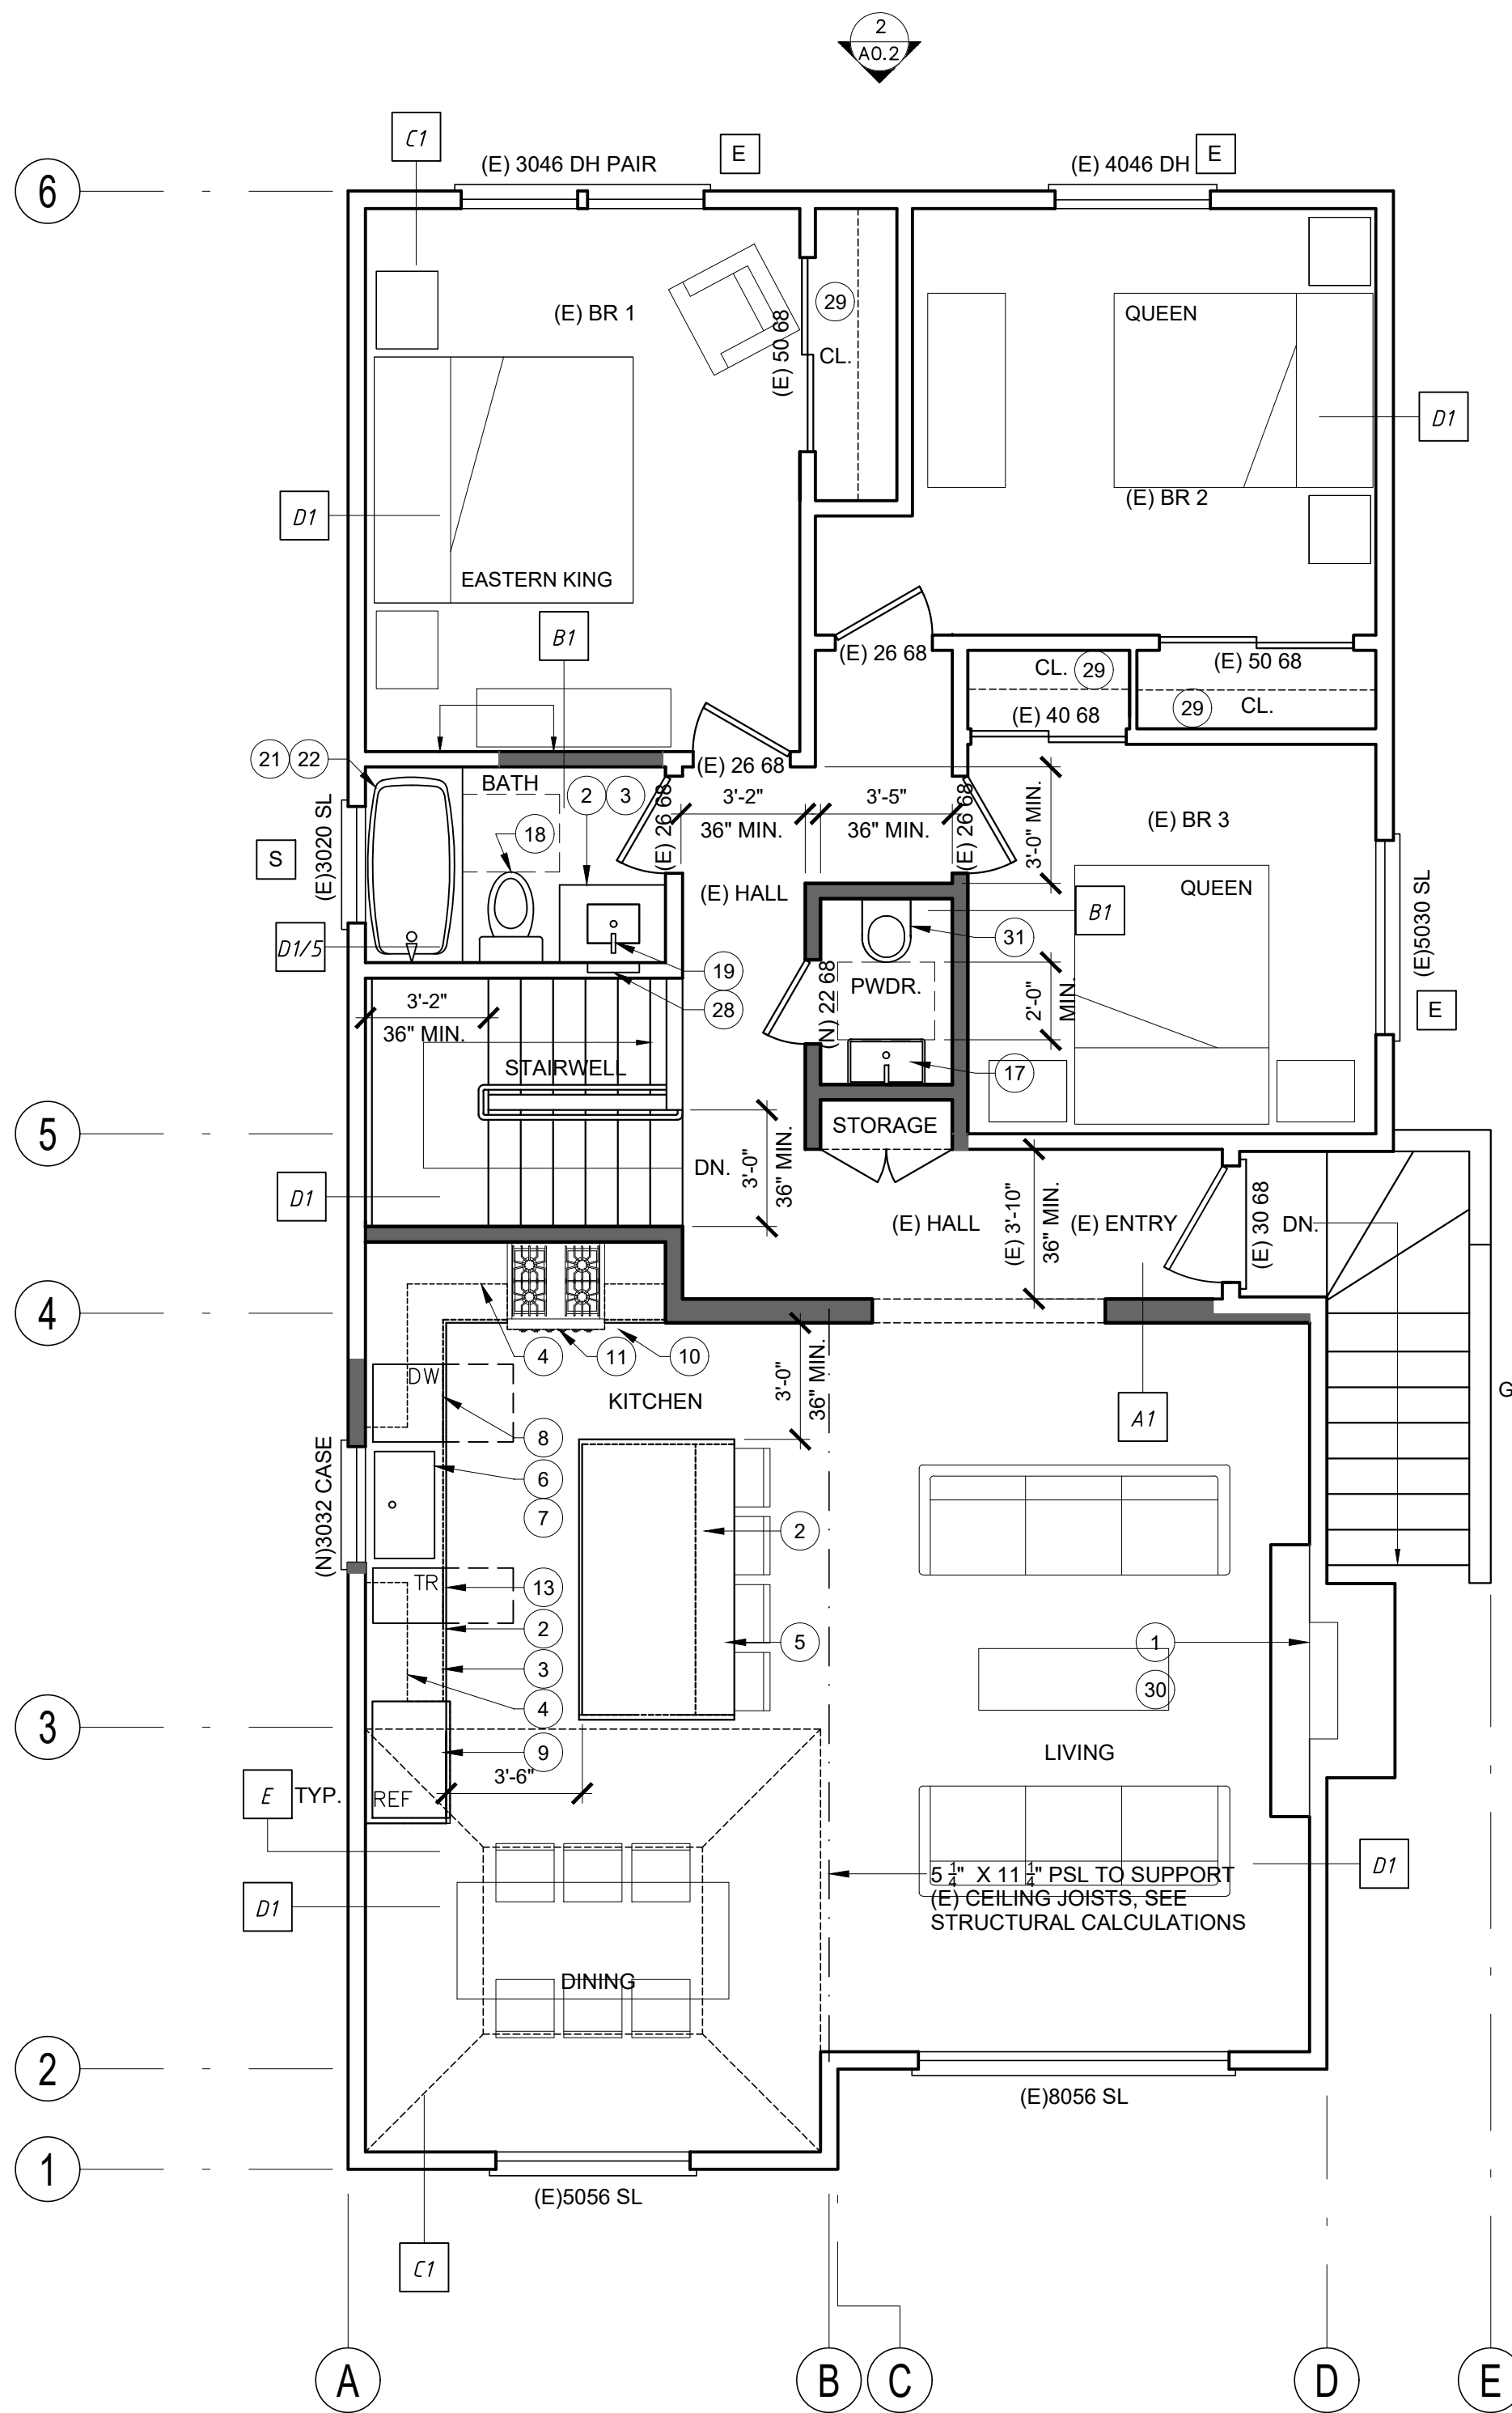
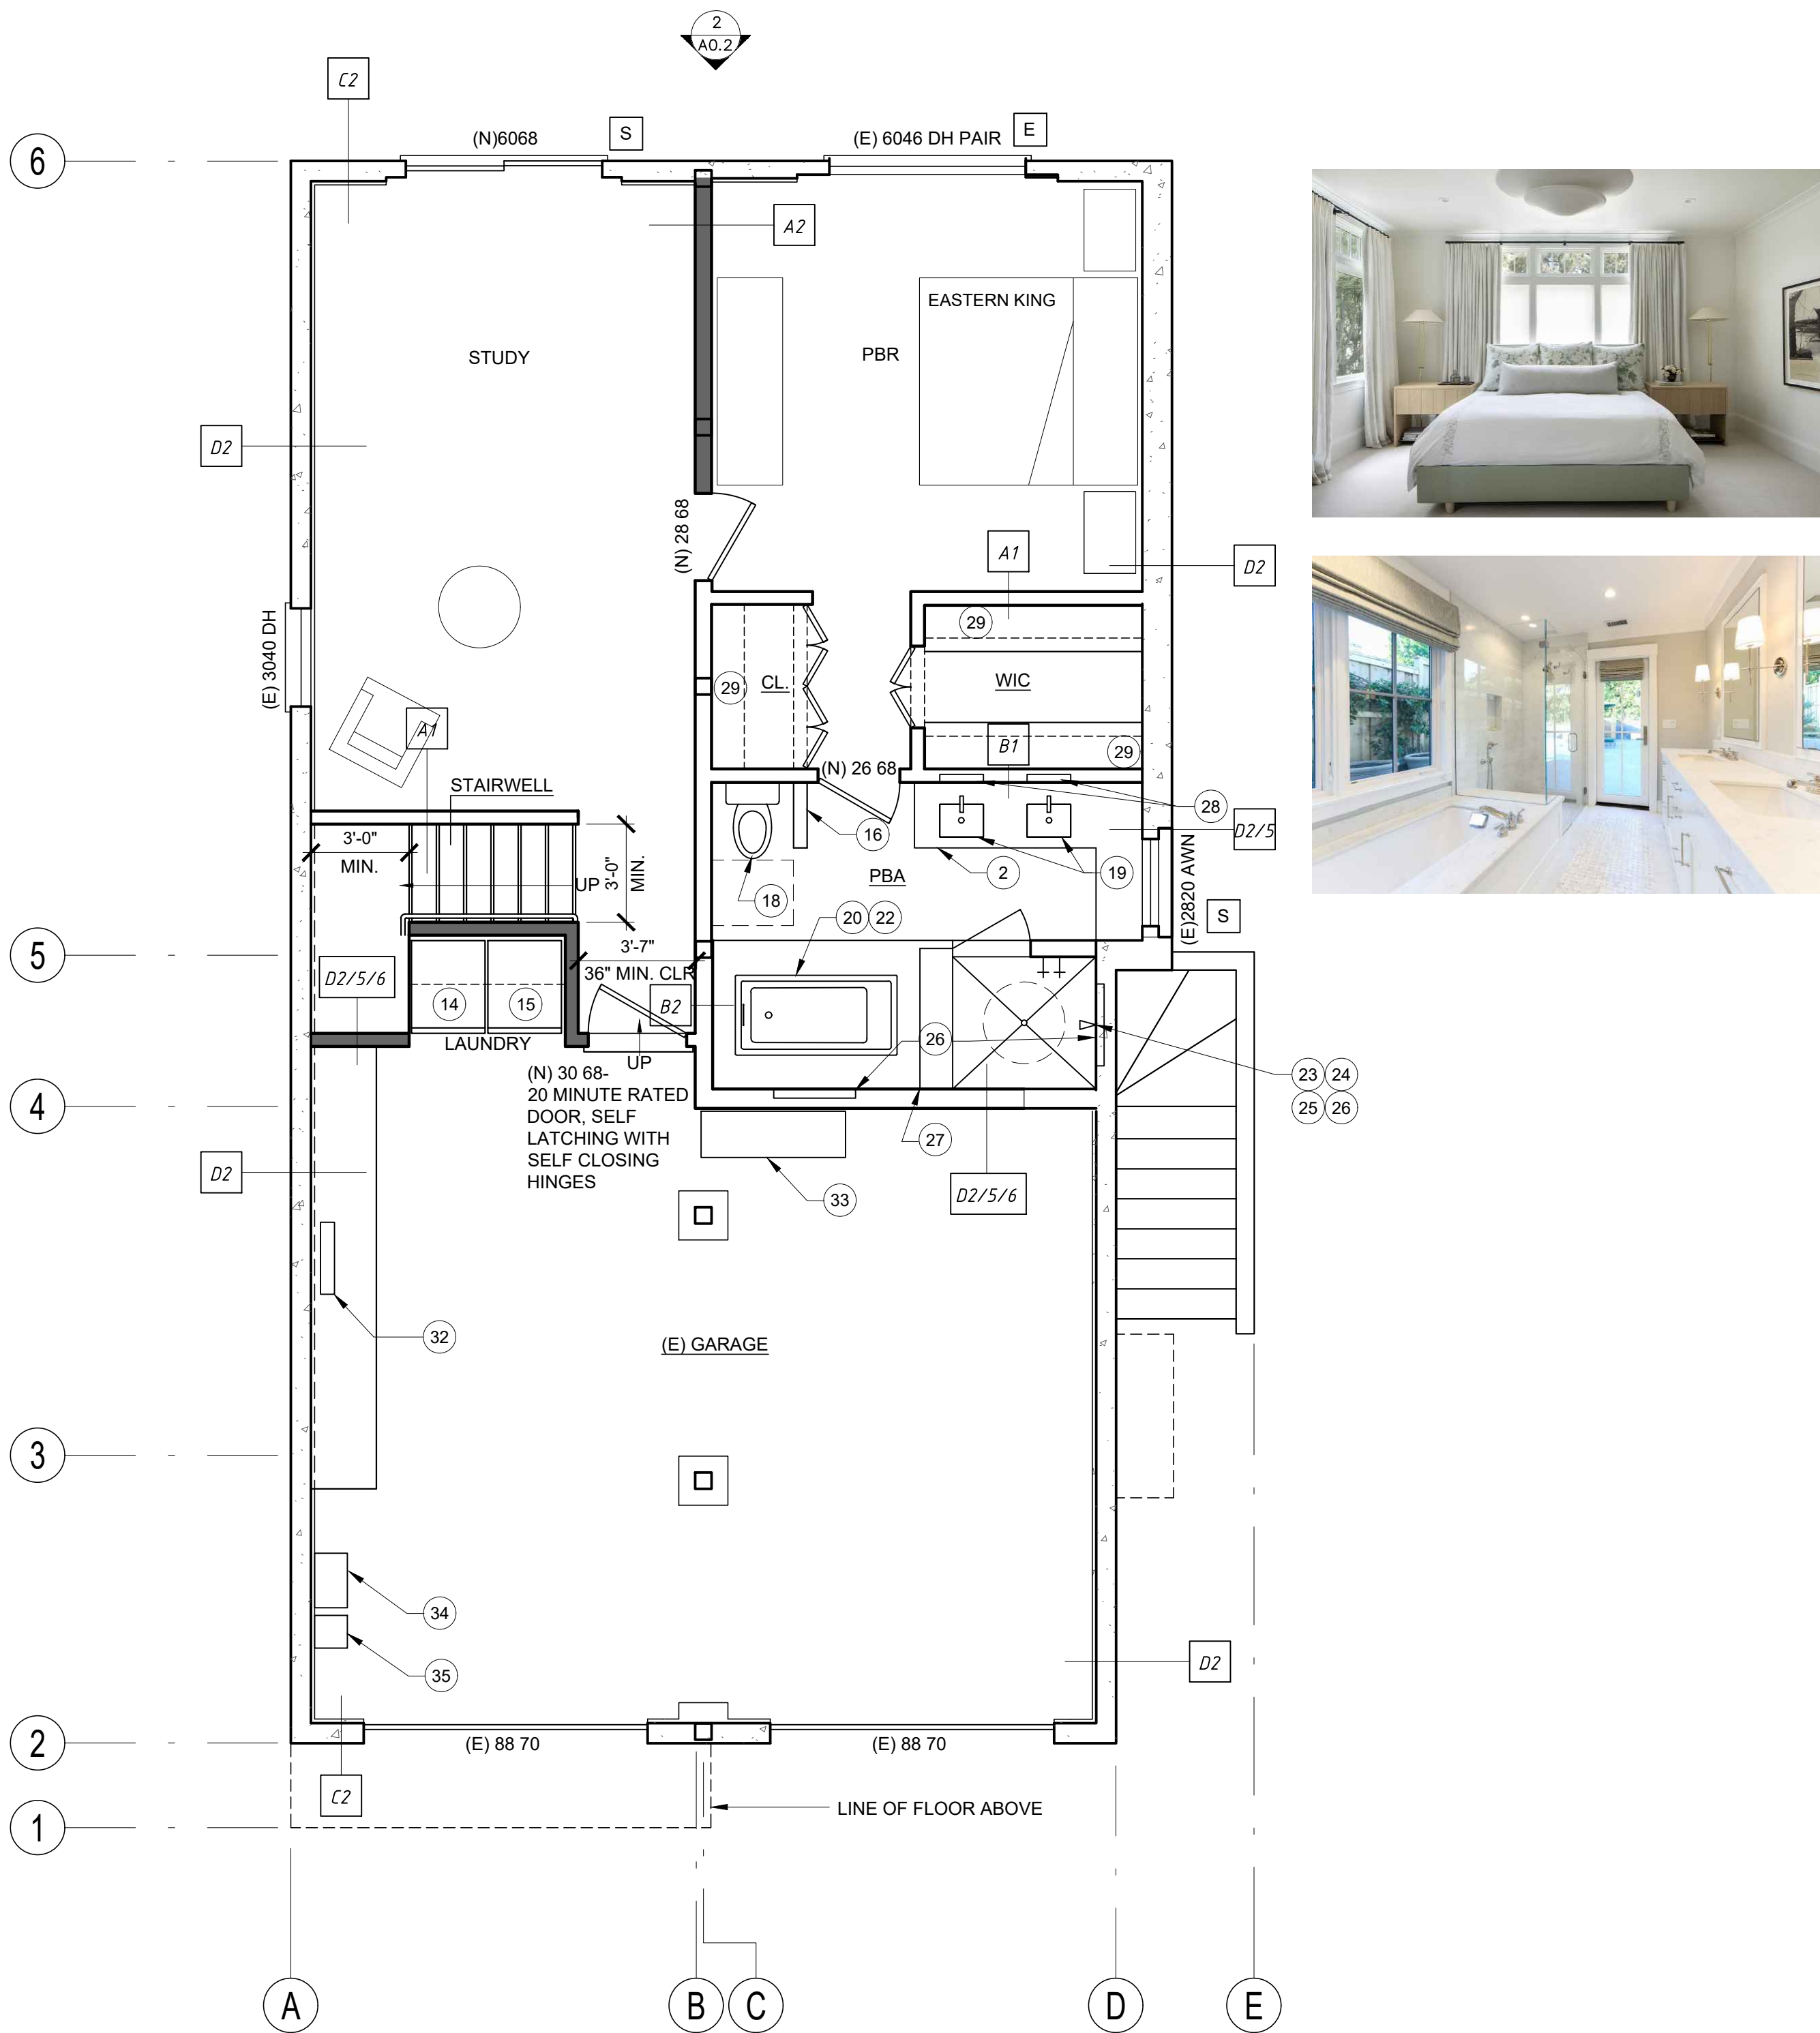
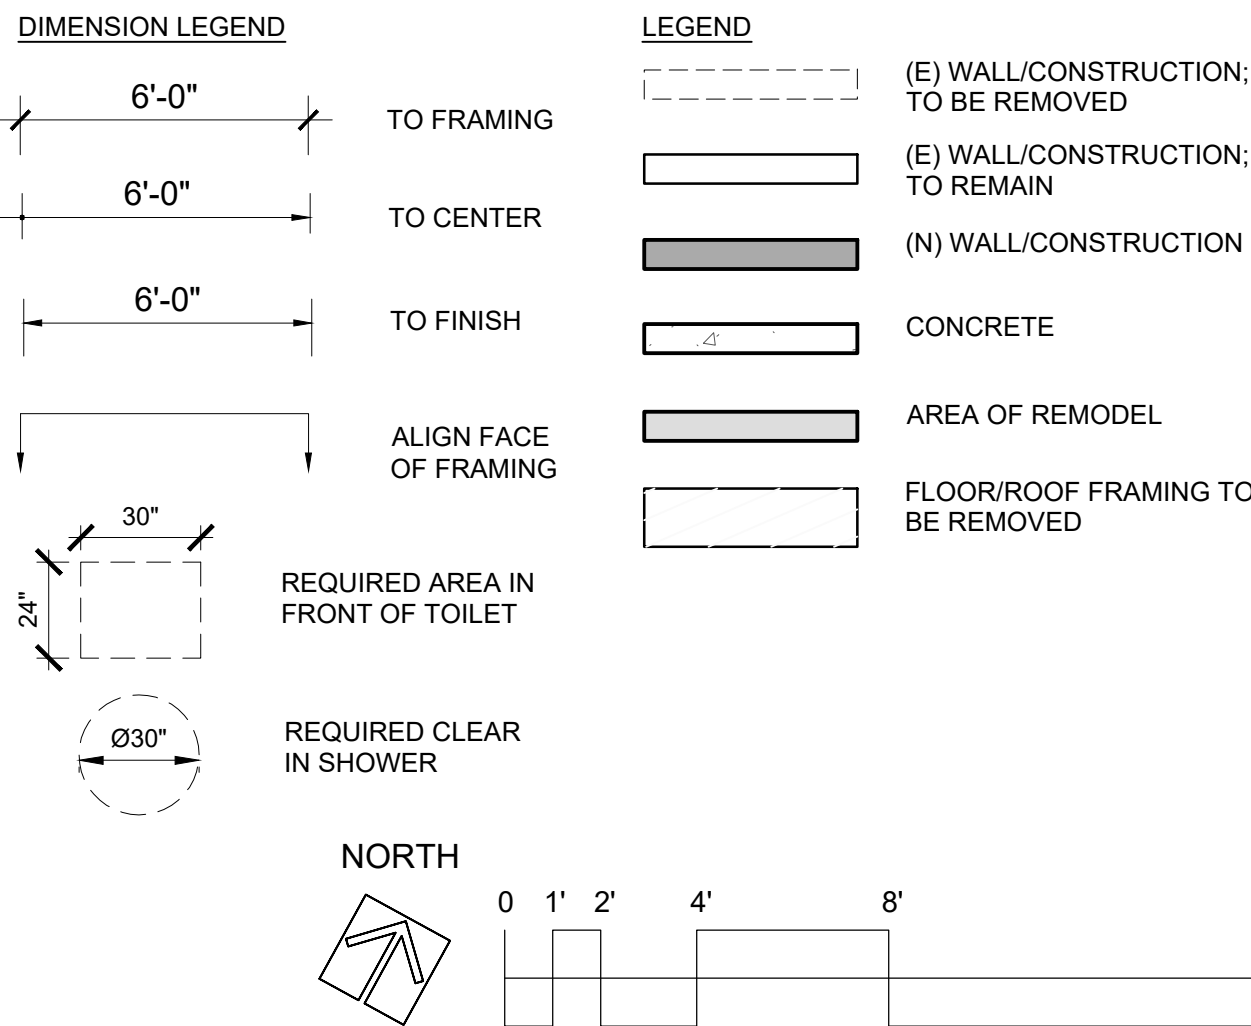


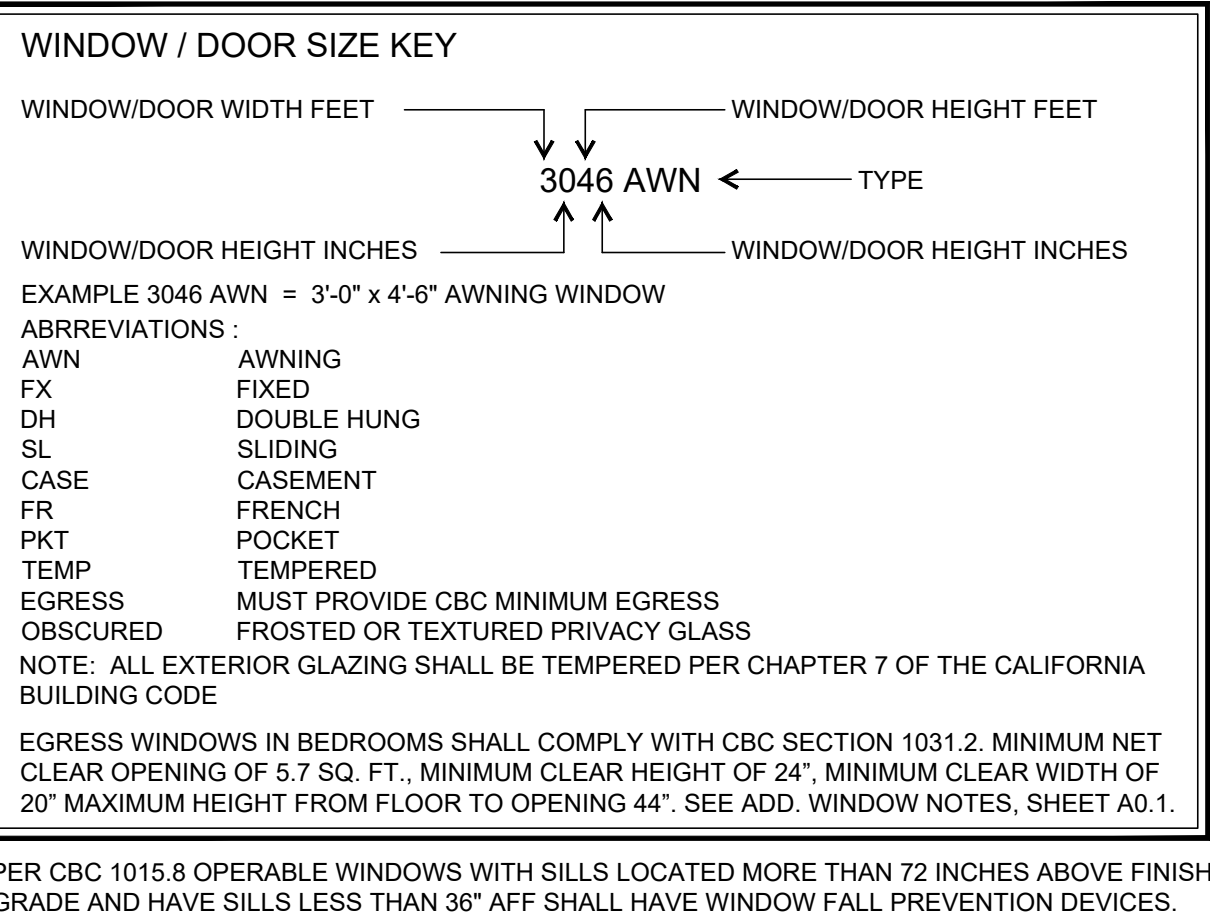

- FLOOR PLAN KEY NOTES:**
- 1 FIREPLACE SURROUND PER OWNER; ARCHITECT TO ADVISE AS REQ'D.
 - 2 SOLID SURFACE COUNTERTOP (+36" AFF)
 - 3 CABINETS (LOWER; FULL HEIGHT NOTED)
 - 4 UPPER CABINETS
 - 5 ISLAND WITH SEATING
 - 6 KITCHEN SINK WITH GARBAGE DISPOSAL
 - 7 KITCHEN FAUCET
 - 8 DISHWASHER
 - 9 REFRIGERATOR/FREEZER
 - 10 RANGE
 - 11 KITCHEN EXHAUST HOOD
 - 12 MICROWAVE
 - 13 TRASH/RECYCLING STATION
 - 14 WASHER
 - 15 DRYER
 - 16 HALF WALL
 - 17 WALL MOUNTED SINK
 - 18 TOILET
 - 19 LAVATORY WITH FAUCET
 - 20 BATHTUB
 - 21 BATHTUB, BUILT IN, ALCOVE
 - 22 BATH CONTROLS/SPOUT
 - 23 THERMOSTATIC CONTROL, TRIM KIT
 - 24 SHOWER HEAD
 - 25 HANDHELD SHOWER HEAD
 - 26 NICHE, CONFIRM SIZE WITH OWNER
 - 27 GLASS SHOWER ENCLOSURE
 - 28 RECESSED MEDICINE CABINET, VIF WITH OWNER
 - 29 CLOSET SHELVE/POLE
 - 30 WALL HUNG TELEVISION
 - 31 WALL MOUNTED TOILET (TOTO)
 - 32 ON DEMAND WATER HEATER
 - 33 HVAC, SEE MEP NOTES
 - 34 (E) GAS METER
 - 35 (E) ELECTRIC METER
- GENERAL FLOOR PLAN NOTES:**
1. CONTRACTOR SHALL BE RESPONSIBLE FOR CONSTRUCTION CONFORMANCE WITH THE APPROVED PLANS, SPECIFICATIONS, AND ALL CODE REQUIREMENTS UNDER WHICH THE PLANS AND SPECIFICATIONS WERE APPROVED.
 2. ALL CONSTRUCTION SHALL COMPLY WITH THE 2022 CALIFORNIA BUILDING CODE, 2022 CALIFORNIA RESIDENTIAL CODE, 2022 CALIFORNIA MECHANICAL, PLUMBING, AND ELECTRICAL CODES, AND ALL LOCAL CODES AND ORDINANCES.
 3. ALL DIMENSIONS AND EXISTING CONDITIONS SHALL BE CHECKED AND FIELD VERIFIED BY THE CONTRACTOR BEFORE PROCEEDING WITH THE WORK.
 4. DO NOT SCALE THESE DRAWINGS. IF THE DRAWINGS ARE NOT 24" X 36", THEY HAVE BEEN REDUCED OR ENLARGED.
 5. REFER TO STRUCTURAL DRAWINGS FOR ADDITIONAL INFORMATION.
 6. ALL NOTES DESCRIBE NEW CONDITIONS UNLESS OTHERWISE NOTED AS (E) OR EXISTING.
 7. COORDINATE ALL MECHANICAL, PLUMBING, AND ELECTRICAL DEVICES WITH SCHEDULES AND REFLECTED CEILING PLANS.
 8. ALL PIPING, VENTS, AND FLUES THAT PENETRATE THE ROOF ARE TO BE LOCATED AND APPROVED BY THE ARCHITECT. VERIFY LOCATIONS PRIOR TO INSTALLATION.
 9. PROVIDE APPROVED BACKER BOARD (ANSI A118.9 OR ASTM C 1325) OR MORTAR BED PER TCA METHOD B411 OR B414, UNDER TILE AT SHOWER TO A HEIGHT OF 72" MINIMUM ABOVE THE DRAIN INLET.
 10. PROVIDE 24 GAUGE COPPER FLASHING AT ALL EXTERIOR OPENINGS.
 11. PROVIDE INSULATION IN ROOF, WALLS, AND FLOORS
 12. PROVIDE 15# FELD UNDER ALL EXTERIOR SIDING.
 13. PROVIDE FIRE BLOCKING AT ALL CEILINGS, FLOORS, FURRED DOWN CEILINGS, SHOWERS AND AT CONCEALED DRAFT OPENINGS NOT TO EXCEED 10 FEET MAX.
 14. ALL INTERIOR DOORS TO MATCH EXISTING 1-3/4" PAINT GRADE SOLID CORE WOOD DOORS.
 15. PER CBC 406.3.2.1, GARAGE SHALL BE SEPARATED FROM THE DWELLING UNIT BY MEANS OF GYPSUM BOARD, NOT LESS THAN 1/2 INCH IN THICKNESS, APPLIED TO THE GARAGE SIDE. GARAGES BENEATH HABITABLE ROOM SHALL BE SEPARATED FROM ALL HABITABLE ROOMS ABOVE BY NOT LESS THAN A 5/8 INCH TYPE "X" GYPSUM BOARD OR EQUIVALENT AND 1/2 INCH GYPSUM BOARD APPLIED TO STRUCTURES SUPPORTING THE SEPARATION FROM HABITABLE ROOMS ABOVE THE GARAGE. DOOR OPENINGS BETWEEN PRIVATE GARAGE AND DWELLING UNIT SHOULD BE EQUIPPED WITH EITHER SOLID WOOD DOORS OR SOLID OR HONEYCOMB CORE STEEL DOORS NOT LESS THAN ONE AND 1-3/8 INCHES IN THICKNESS OR DOORS IN COMPLIANCE WITH SECTION 716.2.2.1 WITH A FIRE PROTECTION RATING OF NOT LESS THAN 20 MINUTES. DOORS SHALL BE SELF CLOSING AND SELF LATCHING.

PARTITION TYPES: --

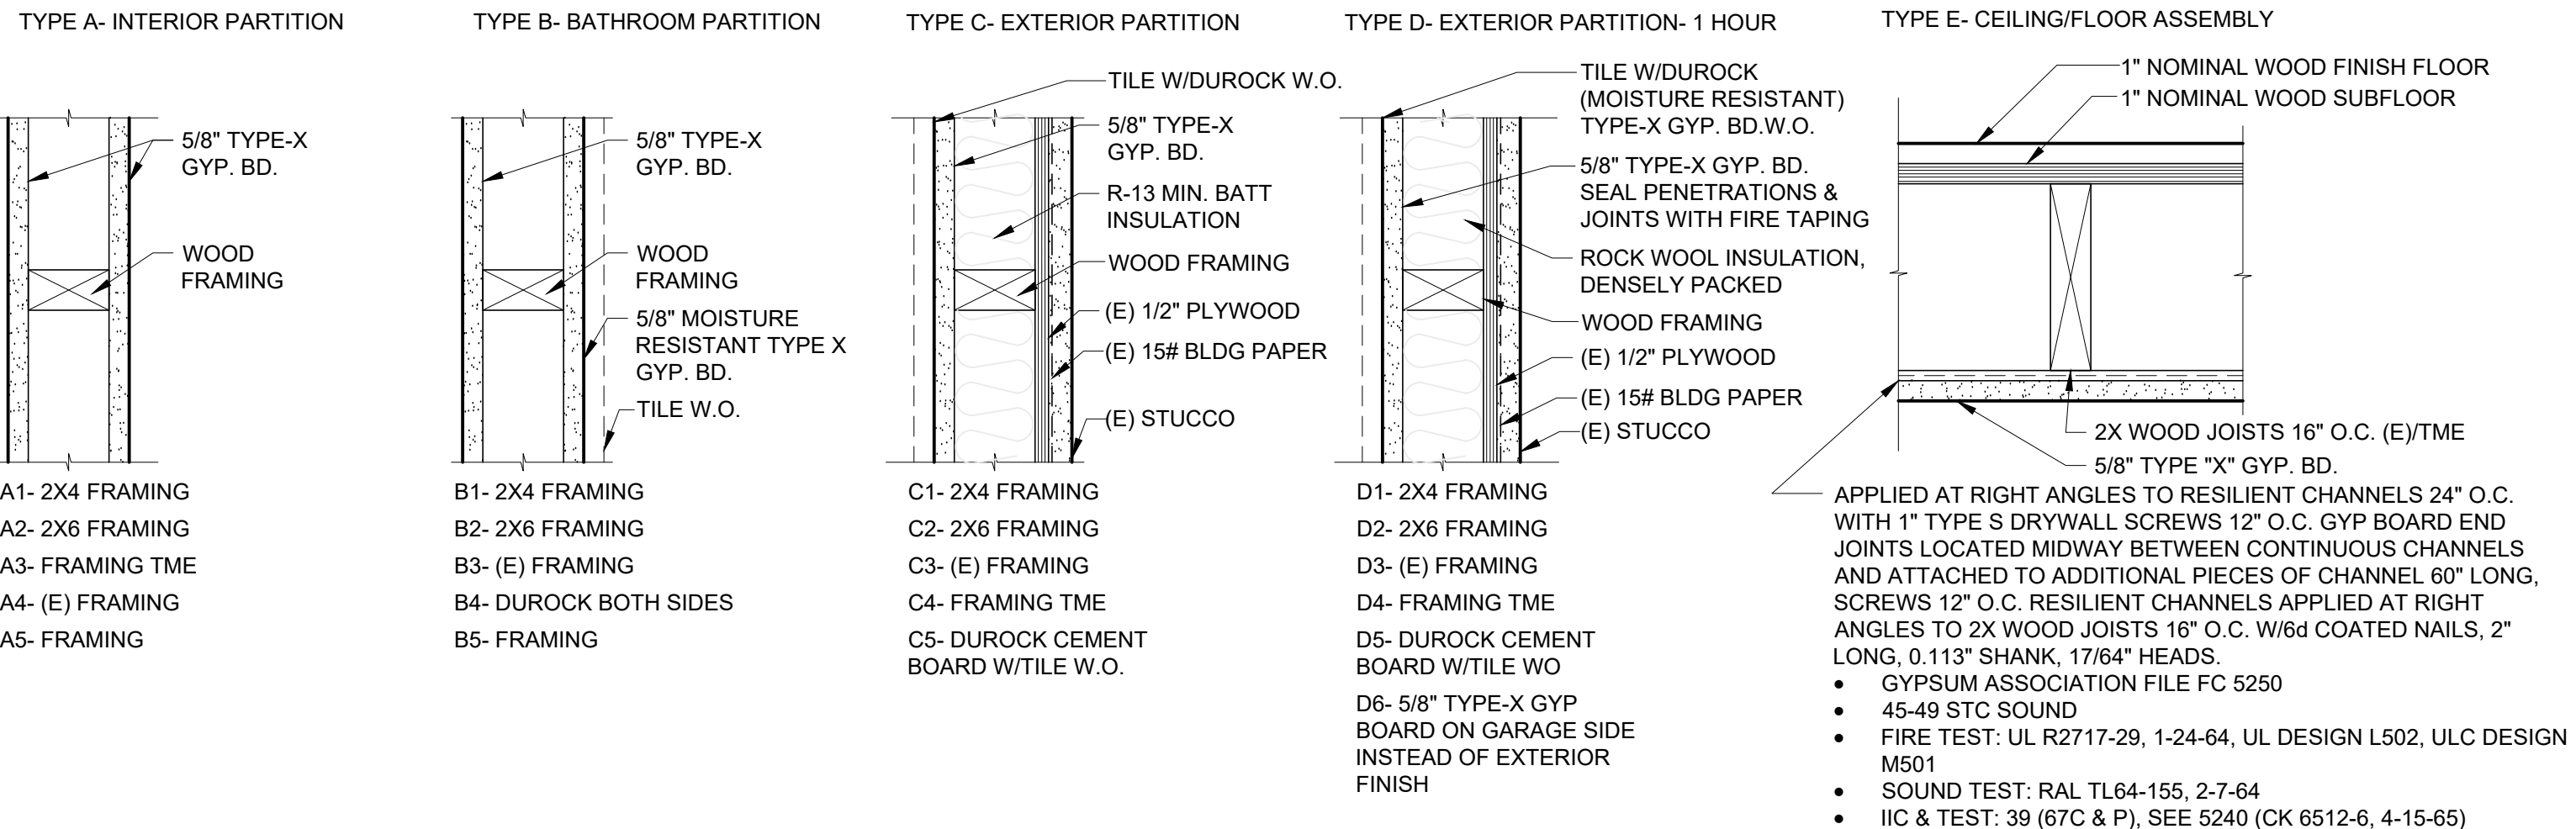

PATRICK HUNTER architect



1125 IDYLBERRY ROAD
SAN RAFAEL, CA 94903

415 | 302 | 7234

DATE and DESCRIPTION
APRIL 28, 2025 - 1
PERMIT RESUBMITTAL

PROJECT

DAVIS RESIDENCE
41 CLAIRVIEW COURT
SAN FRANCISCO, California
Block: 2783 Lot: 003

DOCUMENT DISCLAIMER & COPYRIGHT

Do not scale these drawings. All Dimensions to be checked and verified on site.

All omissions and discrepancies are to be reported to the architect immediately.

These drawings are copyrighted and instruments of service of Patrick Hunter Architect. Information on these drawings is to be used exclusively for the intended project. Patrick Hunter Architect assumes no responsibility for the information contained on these drawings when used and/or modified by others.

Copyright 2025, Patrick Hunter Architect

DRAWN BY: PH/cgg
JOB NO.: 2420
DATE: JUNE 12, 2025
SCALE: 1/4" = 1'-0"

PROPOSED FLOOR PLANS

SHEET NO.:

A2.0

PROPOSED FLOOR PLANS

1